Der Plan als Sprache des Architekten

•Der Plan als eine unverständliche Architektensprache ??

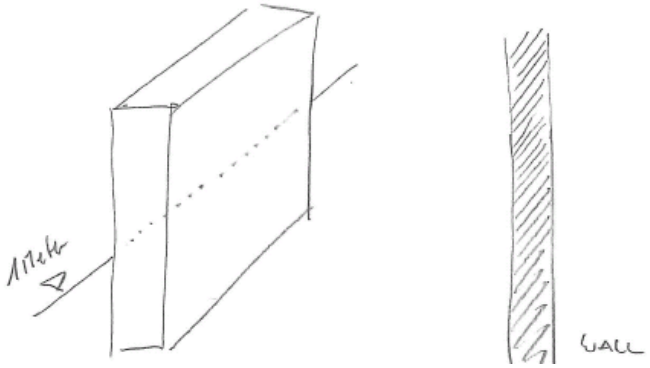

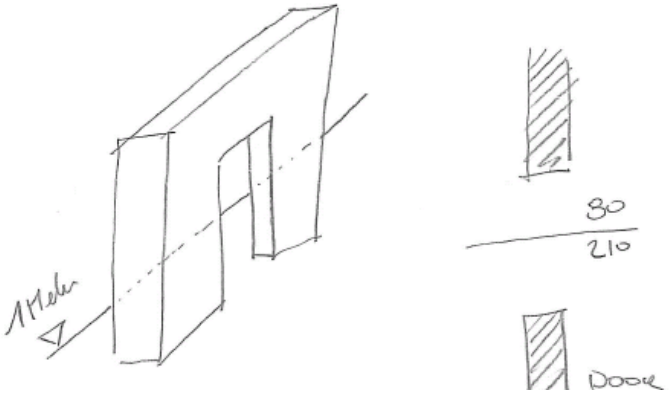

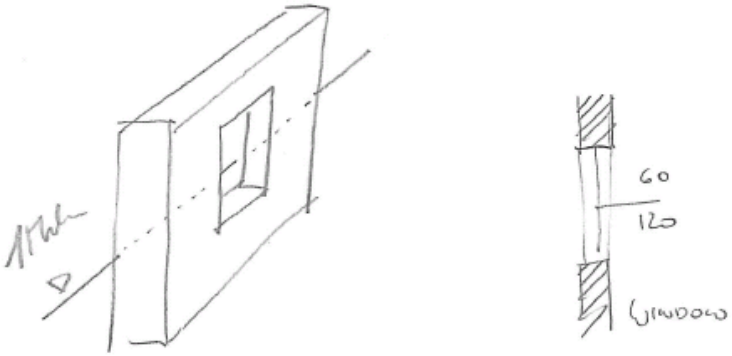

…… und eigentlich ist alles ganz einfach !!!!

Der Plan als Sprache des Architekten

•Die Zeichnung als Kommunikationsmittel des Planers zum Auftraggeber

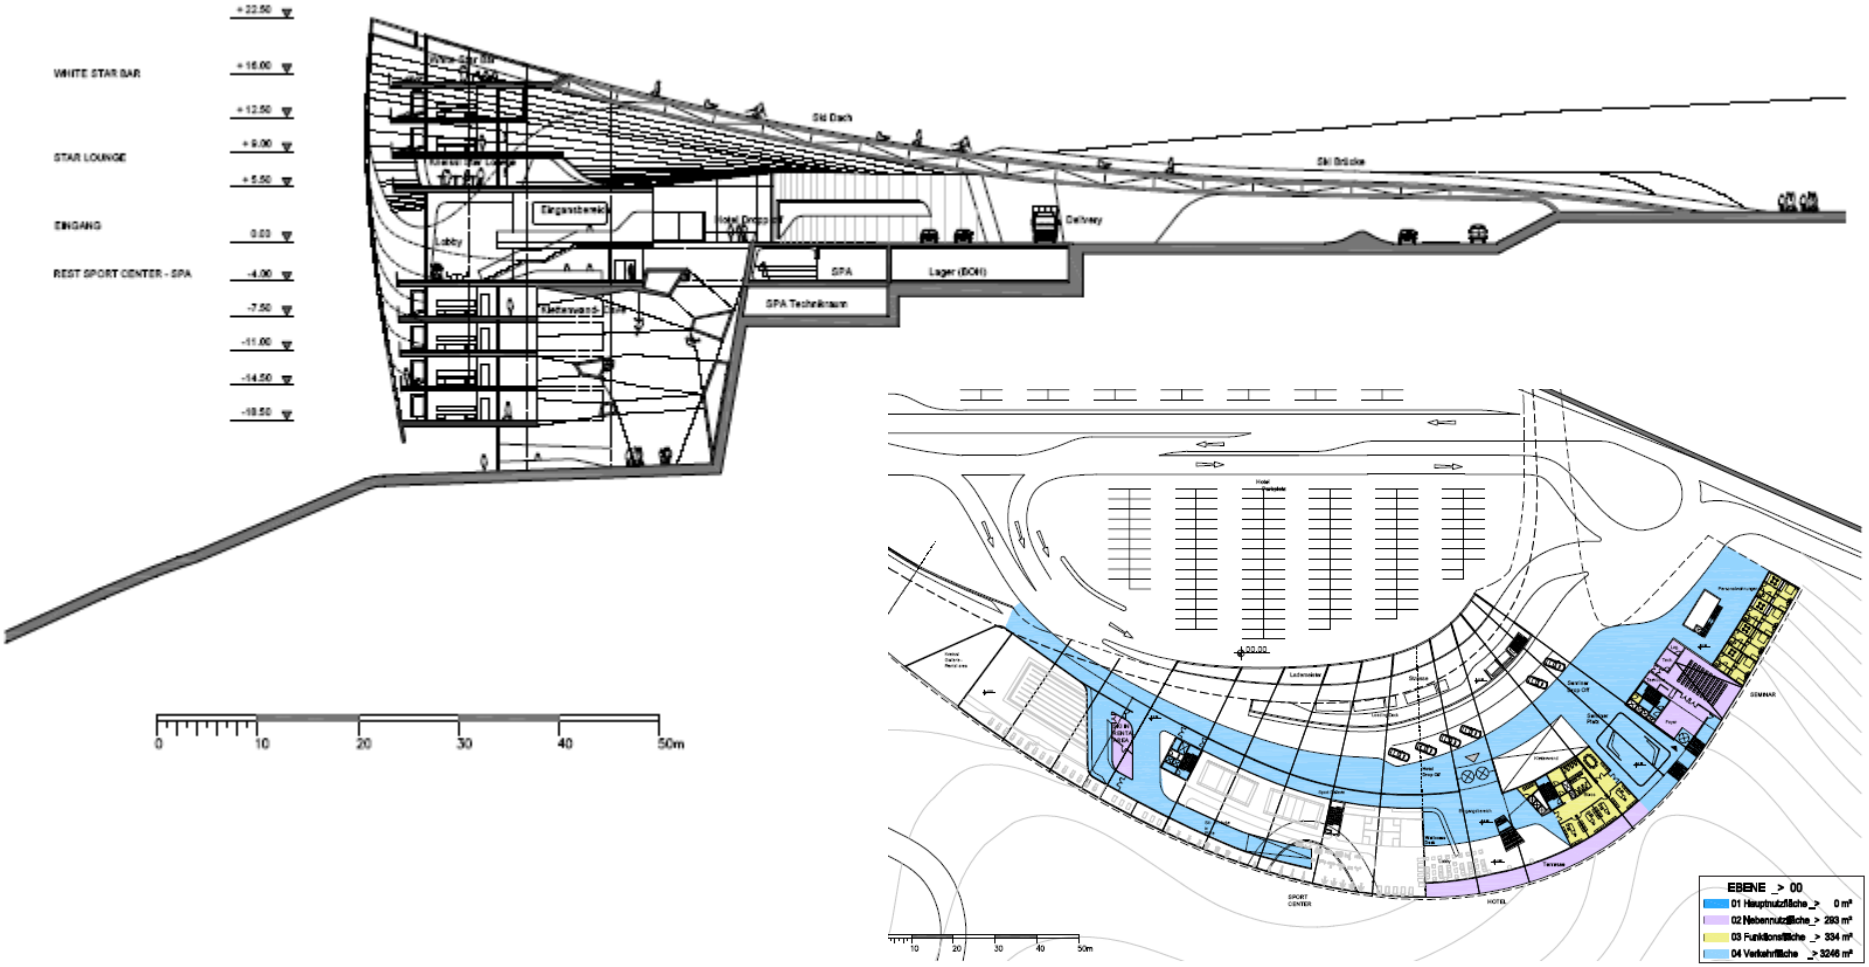

Der Plan als Sprache des Architekten

•Der Plan als eine unverständliche Architektensprache ??

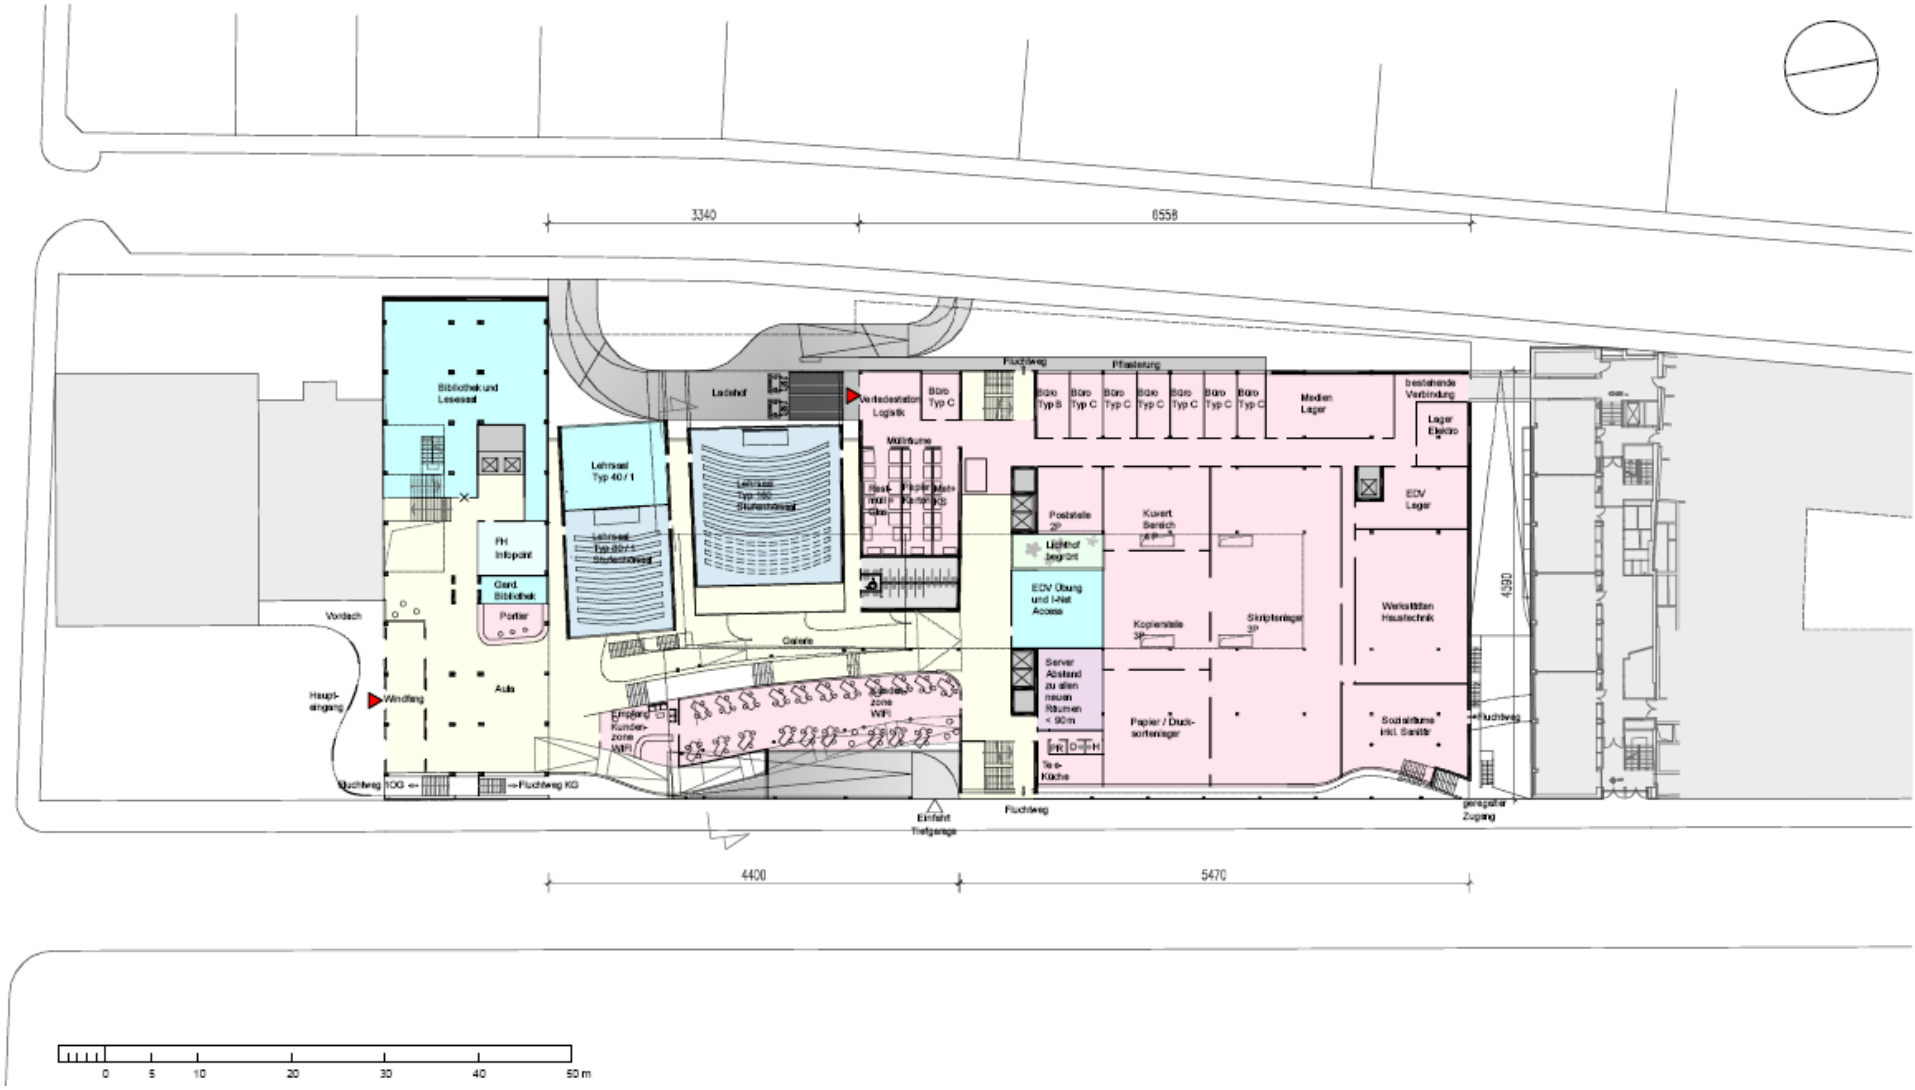

Planinhalte

DK 1. 1993

Technische Zeichnungen für den Hochbau
Kennzeichnung, Bemaßung und Darstellung

ÖNORM A 6240-2

Technical drawings for building construction – Indication, dimensioning and presentation

Dessins techniques pour la construction immobilière – Marquage, cotation et présentation

Auch Normengruppen A1 und B

Ersatz für ÖNORMEN
A 6240-6:1980 bis
A 6240-9:1980

1	**Anwendungsbereich**	2
2	**Abkürzung von in Plänen verwendeten Bezeichnungen**	2
3	**Bezeichnung von Gebäuden, Geschoßen und Räumen**	3
4	**Lagefestlegung in Gebäuden mit Hilfe von Rasterlinien oder Netzlinien**	3
5	**Bemaßung**	5
6	**Kennzeichnung von Baustoffen**	15
7	**Darstellung von Bauteilen, Bauteilöffnungen, Einbauteilen und Hausinstallationseinrichtungen**	16
7.1	Stiegen	16
7.2	Rampen	16
7.3	Aufzüge	16
7.4	Fahrtreppen und Fahrsteige	18
7.5	Fensteröffnungen, Fensterstöcke	18
7.6	Türöffnungen, Türstöcke	18
7.7	Rauch-, Abgas- und Luftfänge	18
7.8	Durchbrüche und Aussparungen	20
7.9	Darstellungen von Ver- und Entsorgungseinrichtungen	24
7.10	Darstellung von Entwässerungsanlagen (Kanalisation)	25
8	**Darstellung von Neu-, Zu- und Umbauten in Einreichplänen**	26
9	**Darstellung von Neu-, Zu- und Umbauten in Ausführungsplänen**	28
10	**Bezugsnormen**	29
11	**Hinweis auf andere Unterlagen**	29

Planinhalte

1 Anwendungsbereich

Die ÖNORM A 6240 regelt alle die Plandarstellung betreffenden Bereiche von technischen Zeichnungen des Hochbaues und verwandter, raumbildender Konstruktionen des Tiefbaues.

In Teil 1 werden die wichtigsten Begriffsbestimmungen und allgemeine Regeln über die Blattgestaltung festgelegt.

Teil 2 enthält bauplanbezogene Hinweise, Kennzeichnungen und Abkürzungen sowie die Darstellungsarten für verschiedene Bauteile und Baupläne.

2 Abkürzungen von in Plänen verwendeten Bezeichnungen

In Bauzeichnungen werden für oft eingetragene Bezeichnungen Abkürzungen verwendet. In dieser ÖNORM sind nur diejenigen Abkürzungen enthalten, die allgemein gebräuchlich und ohne besondere Legende verständlich sind. Seltene Planungsbegriffe sollen entweder nicht abgekürzt oder erforderlichenfalls mit freien, in einer Legende zu erläuternden Abkürzungen gekennzeichnet werden. Die Gleichheit mit anderen in derselben Zeichnung oder in dieser ÖNORM verwendeten Abkürzungen ist zu vermeiden.

2.1 Geschoßbezeichnungen

EG ..... Erdgeschoß
OG ..... Obergeschoß (1., 2., 3.,)
ST ..... Stockwerk (1., 2., 3.,)
UG ..... Untergeschoß (1., 2., 3.,)
DG ..... Dachgeschoß
KG ..... Kellergeschoß

2.2 Ordnungsbezeichnungen

ON ..... Orientierungsnummer
POS ..... Positionsnummer
TOP ..... topographische Nummer
EZ ..... Einlagezahl
GST ..... Grundstücksnummer
KG ..... Katastralgemeinde

2.3 Raumwidmung

Wenn die Raumwidmung nicht ausgeschrieben wird, sind folgende Abkürzungen zu verwenden:

WF ..... Windfang
VR ..... Vorraum
G ..... Gang
DI ..... Diele
BAD ..... Badezimmer
WR ..... Waschraum
WK ..... Waschküche
WC ..... Abort (Wasserclosett)
KÜ ..... Küche
KN ..... Kochnische
AR ..... Abstellraum
SP ..... Speisekammer
SR ..... Schrankraum
GA ..... Garage
ZI ..... Zimmer (Aufenthaltsraum mit mindestens 10 m²)
KA ..... Kabinett, Kammer (Aufenthaltsraum kleiner als 10 m²)

2.4 Höhenbezugs- und Maßangaben

OK, OS : Oberkante[1]), Oberseite,
UK, US : Unterkante, Unterseite,
DOK, DOS : Deckenoberkante, Deckenoberseite (Rohbaumaß)
DUK, DUS : Deckenunterkante, Deckenunterseite (Rohbaumaß)
FBOK, OFF : Fußbodenoberkante, Oberfläche des fertigen Fußbodens
FDOK, FDOS : Fundamentoberkante, Fundamentoberseite)
FDUK, FDUS : Fundamentunterkante, Fundamentunterseite)
STUK : Sturzunterkante (Rohbaumaß)
STH : Sturzhöhe, gemessen von STUK bis DUK (Rohbaumaß)
RPH : Rohbauparapethöhe (gemessen von FBOK)
FPH : fertige Parapethöhe, gemessen von FBOK bis Oberkante des inneren Fensterbretts

2.5 Öffnungen und deren Abschlüsse

WD ..... Wanddurchbruch
DD ..... Deckendurchbruch
FBD ..... Fußbodendurchbruch
FDD ..... Fundamentdurchbruch
WS ..... Wandschlitz
WA ..... Wandaussparung
DA ..... Deckenaussparung
FBA ..... Fußbodenaussparung
RBL ..... Rohbaulichte
AL ..... Architekturlichte
STL ..... Stocklichte
GL ..... Glaslichte
STAM ..... Stockaußenmaß
DF ..... Drehflügel
DKF ..... Drehkippflügel
SF ..... Schiebeflügel
SWF ..... Schwingflügel
WF ..... Wendeflügel
HT ..... Hebetüre
HST ..... Hebeschiebetüre
T 30, T 60, T 90 ..... Brandschutztüren mit Angabe der Brandwiderstandsklasse (siehe ÖNORM B 3850)
GT ..... gasdichte Türe
R 30 ..... rauchdichte Türe (siehe ÖNORM B 3855)
DT ..... Drucktüre

2.6 Rauch-, Abgas- und Luftfänge, Schächte

L ..... Lüftungsschacht
PT ..... Putztürchen
KT ..... Kehrtürchen
ABL ..... Abluft
ZUL ..... Zuluft
M ..... Müllabwurfschacht

geschoßweise Fangzuordnung (Bezeichnung des zugehörigen Anschlußgeschoßes, siehe auch ÖNORM B 8208):

K ..... Keller
E ..... Erdgeschoß
1 ..... 1. Obergeschoß (1. Stock)
2 ..... 2. Obergeschoß (2. Stock)
D ..... Dachgeschoß

[1]) Der Begriff "Oberkante" wurde als synonymer Begriff für "Oberseite" in dieser Norm belassen, weil er sehr verbreitet ist und in der Schnittdarstellung der Schnittkante zwischen Oberseite und Schnittebene entspricht.

2.1 Geschoßbezeichnungen

EG ..... Erdgeschoß
OG ..... Obergeschoß (1., 2., 3.,)
ST ..... Stockwerk (1., 2., 3.,)
UG ..... Untergeschoß (1., 2., 3.,)
DG ..... Dachgeschoß
KG ..... Kellergeschoß

2.3 Raumwidmung

Wenn die Raumwidmung nicht ausgeschrieben wird, sind folgende Abkürzungen zu verwenden:

WF ..... Windfang
VR ..... Vorraum
G ..... Gang
DI ..... Diele
BAD ..... Badezimmer
WR ..... Waschraum
WK ..... Waschküche
WC ..... Abort (Wasserclosett)
KÜ ..... Küche
KN ..... Kochnische
AR ..... Abstellraum
SP ..... Speisekammer
SR ..... Schrankraum
GA ..... Garage
ZI ..... Zimmer (Aufenthaltsraum mit mindestens 10 m²)
KA ..... Kabinett, Kammer (Aufenthaltsraum kleiner als 10 m²)

Planinhalte

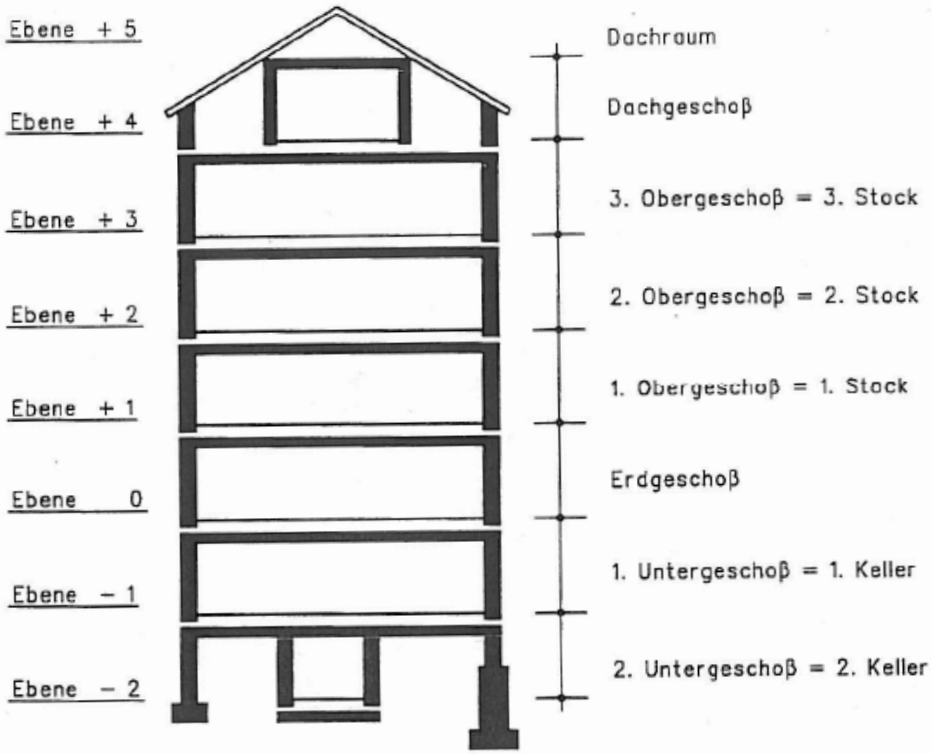

Bild 1

Diese Numerierung ist nach Bauteil-, Stiegen-, Geschoß-, Wohnungs- oder Raumnummer benannt.

Beispiele: 708 : 7. Stock, Raum 8
E 32 : Erdgeschoß, Raum 32

Planinhalte

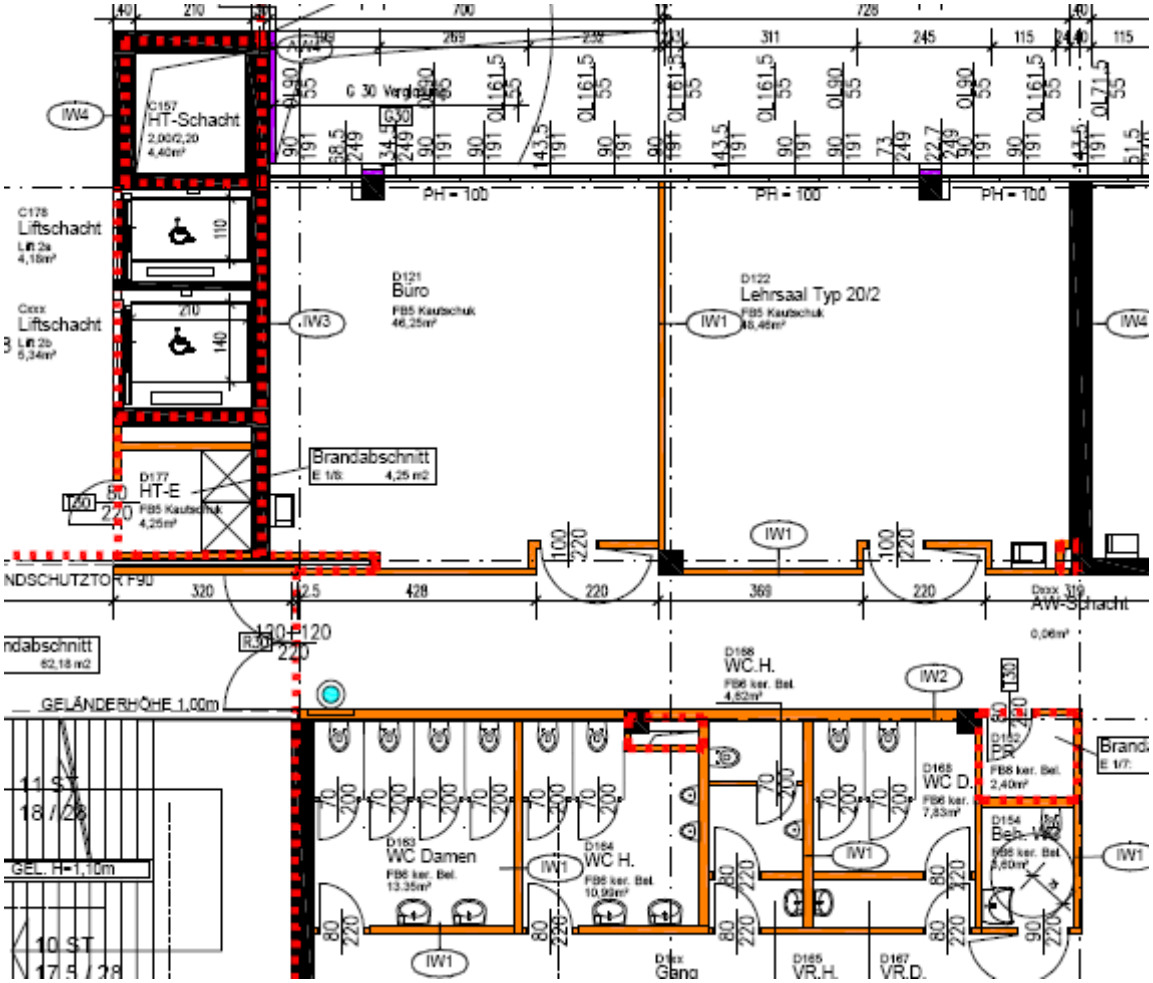

Planinhalte

1 Anwendungsbereich

Die ÖNORM A 6240 regelt alle die Plandarstellung betreffenden Bereiche von technischen Zeichnungen des Hochbaues und verwandter, raumbildender Konstruktionen des Tiefbaues.

In Teil 1 werden die wichtigsten Begriffsbestimmungen und allgemeine Regeln über die Blattgestaltung festgelegt.

Teil 2 enthält bauplanbezogene Hinweise, Kennzeichnungen und Abkürzungen sowie die Darstellungsarten für verschiedene Bauteile und Baupläne.

2 Abkürzungen von in Plänenverwendeten Bezeichnungen

In Bauzeichnungen werden für oft eingetragene Bezeichnungen Abkürzungen verwendet. In dieser ÖNORM sind nur diejenigen Abkürzungen enthalten, die allgemein gebräuchlich und ohne besondere Legende verständlich sind. Seltene Planungsbegriffe sollen entweder nicht abgekürzt oder erforderlichenfalls mit freien, in einer Legende zu erläuternden Abkürzungen gekennzeichnet werden. Die Gleichheit mit anderen in derselben Zeichnung oder in dieser ÖNORM verwendeten Abkürzungen ist zu vermeiden.

2.1 Geschoßbezeichnungen

EG ..... Erdgeschoß
OG ..... Obergeschoß (1., 2., 3.,)
ST ..... Stockwerk (1., 2., 3.,)
UG ..... Untergeschoß (1., 2., 3.,)
DG ..... Dachgeschoß
KG ..... Kellergeschoß

2.2 Ordnungsbezeichnungen

ON ..... Orientierungsnummer
POS ..... Positionsnummer
TOP ..... topographische Nummer
EZ ..... Einlagezahl
GST ..... Grundstücksnummer
KG ..... Katastralgemeinde

2.3 Raumwidmung

Wenn die Raumwidmung nicht ausgeschrieben wird, sind folgende Abkürzungen zu verwenden:

WF ..... Windfang
VR ..... Vorraum
G ..... Gang
DI ..... Diele
BAD ..... Badezimmer
WR ..... Waschraum
WK ..... Waschküche
WC ..... Abort (Wasserclosett)
KÜ ..... Küche
KN ..... Kochnische
AR ..... Abstellraum
SP ..... Speisekammer
SR ..... Schrankraum
GA ..... Garage
ZI ..... Zimmer (Aufenthaltsraum mit mindestens 10 m²)
KA ..... Kabinett, Kammer (Aufenthaltsraum kleiner als 10 m²)

2.4 Höhenbezugs- und Maßangaben

OK, OS : Oberkante[1]), Oberseite,
UK, US : Unterkante, Unterseite,
DOK, DOS : Deckenoberkante, Deckenoberseite (Rohbaumaß)
DUK, DUS : Deckenunterkante, Deckenunterseite (Rohbaumaß)
FBOK, OFF : Fußbodenoberkante, Oberfläche des fertigen Fußbodens
FDOK, FDOS : Fundamentoberkante, Fundamentoberseite)
FDUK, FDUS : Fundamentunterkante, Fundamentunterseite)
STUK : Sturzunterkante (Rohbaumaß)
STH : Sturzhöhe, gemessen von STUK bis DUK (Rohbaumaß)
RPH : Rohbauparapethöhe (gemessen von FBOK)
FPH : fertige Parapethöhe, gemessen von FBOK bis Oberkante des inneren Fensterbretts

2.5 Öffnungen und deren Abschlüsse

WD ..... Wanddurchbruch
DD ..... Deckendurchbruch
FBD ..... Fußbodendurchbruch
FDD ..... Fundamentdurchbruch
WS ..... Wandschlitz
WA ..... Wandaussparung
DA ..... Deckenaussparung
FBA ..... Fußbodenaussparung
RBL ..... Rohbaulichte
AL ..... Architekturlichte
STL ..... Stocklichte
GL ..... Glaslichte
STAM ..... Stockaufmaß
DF ..... Drehflügel
DKF ..... Drehkippflügel
SF ..... Schiebeflügel
SWF ..... Schwingflügel
WF ..... Wendeflügel
HT ..... Hebetüre
HST ..... Hebeschiebetüre
T 30, T 60, T 90 ..... Brandschutztüren mit Angabe der Brandwiderstandsklasse (siehe ÖNORM B 3850)
GT ..... gasdichte Türe
R 30 ..... rauchdichte Türe (siehe ÖNORM B 3855)
DT ..... Drucktüre

2.6 Rauch-, Abgas- und Luftfänge, Schächte

L ..... Lüftungsschacht
PT ..... Putztürchen
KT ..... Kehrtürchen
ABL ..... Abluft
ZUL ..... Zuluft
M ..... Müllabwurfschacht

geschoßweise Fangzuordnung (Bezeichnung des zugehörigen Anschlußgeschoßes, siehe auch ÖNORM B 8208):

K ..... Keller
E ..... Erdgeschoß
1 ..... 1. Obergeschoß (1. Stock)
2 ..... 2. Obergeschoß (2. Stock)
D ..... Dachgeschoß

[1]) Der Begriff "Oberkante" wurde als synonymer Begriff für "Oberseite" in dieser Norm belassen, weil er sehr verbreitet ist und in der Schnittdarstellung der Schnittkante zwischen Oberseite und Schnittebene entspricht.

2.4 Höhenbezugs- und Maßangaben

OK, OS : Oberkante[1]), Oberseite,
UK, US : Unterkante, Unterseite,
DOK, DOS : Deckenoberkante, Deckenoberseite (Rohbaumaß)
DUK, DUS : Deckenunterkante, Deckenunterseite (Rohbaumaß)
FBOK, OFF : Fußbodenoberkante, Oberfläche des fertigen Fußbodens
FDOK, FDOS : Fundamentoberkante, Fundamentoberseite)
FDUK, FDUS : Fundamentunterkante, Fundamentunterseite)
STUK : Sturzunterkante (Rohbaumaß)
STH : Sturzhöhe, gemessen von STUK bis DUK (Rohbaumaß)
RPH : Rohbauparapethöhe (gemessen von FBOK)
FPH : fertige Parapethöhe, gemessen von FBOK bis Oberkante des inneren Fensterbretts

Planinhalte

1 Anwendungsbereich

Die ÖNORM A 6240 regelt alle die Plandarstellung betreffenden Bereiche von technischen Zeichnungen des Hochbaues und verwandter, raumbildender Konstruktionen des Tiefbaues.

In Teil 1 werden die wichtigsten Begriffsbestimmungen und allgemeine Regeln über die Blattgestaltung festgelegt.

Teil 2 enthält bauplanbezogene Hinweise, Kennzeichnungen und Abkürzungen sowie die Darstellungsarten für verschiedene Bauteile und Baupläne.

2 Abkürzungen von in Plänenverwendeten Bezeichnungen

In Bauzeichnungen werden für oft eingetragene Bezeichnungen Abkürzungen verwendet. In dieser ÖNORM sind nur diejenigen Abkürzungen enthalten, die allgemein gebräuchlich und ohne besondere Legende verständlich sind. Seltene Planungsbegriffe sollen entweder nicht abgekürzt oder erforderlichenfalls mit freien, in einer Legende zu erläuternden Abkürzungen gekennzeichnet werden. Die Gleichheit mit anderen in derselben Zeichnung oder in dieser ÖNORM verwendeten Abkürzungen ist zu vermeiden.

2.1 Geschoßbezeichnungen

EG ..... Erdgeschoß
OG ..... Obergeschoß (1., 2., 3.,)
ST ..... Stockwerk (1., 2., 3.,)
UG ..... Untergeschoß (1., 2., 3.,)
DG ..... Dachgeschoß
KG ..... Kellergeschoß

2.2 Ordnungsbezeichnungen

ON ..... Orientierungsnummer
POS ..... Positionsnummer
TOP ..... topographische Nummer
EZ ..... Einlagezahl
GST ..... Grundstücksnummer
KG ..... Katastralgemeinde

2.3 Raumwidmung

Wenn die Raumwidmung nicht ausgeschrieben wird, sind folgende Abkürzungen zu verwenden:

WF ..... Windfang
VR ..... Vorraum
G ..... Gang
DI ..... Diele
BAD ..... Badezimmer
WR ..... Waschraum
WK ..... Waschküche
WC ..... Abort (Wasserclosett)
KÜ ..... Küche
KN ..... Kochnische
AR ..... Abstellraum
SP ..... Speisekammer
SR ..... Schrankraum
GA ..... Garage
ZI ..... Zimmer (Aufenthaltsraum mit mindestens 10 m²)
KA ..... Kabinett, Kammer (Aufenthaltsraum kleiner als 10 m²)

2.4 Höhenbezugs- und Maßangaben

OK, OS : Oberkante[1]), Oberseite,
UK, US : Unterkante, Unterseite,
DOK, DOS : Deckenoberkante, Deckenoberseite (Rohbaumaß)
DUK, DUS : Deckenunterkante, Deckenunterseite (Rohbaumaß)
FBOK, OFF : Fußbodenoberkante, Oberfläche des fertigen Fußbodens
FDOK, FDOS : Fundamentoberkante, Fundamentoberseite)
FDUK, FDUS : Fundamentunterkante, Fundamentunterseite)
STUK : Sturzunterkante (Rohbaumaß)
STH : Sturzhöhe, gemessen von STUK bis DUK (Rohbaumaß)
RPH : Rohbauparapethöhe (gemessen von FBOK)
FPH : fertige Parapethöhe, gemessen von FBOK bis Oberkante des inneren Fensterbretts

2.5 Öffnungen und deren Abschlüsse

WD ..... Wanddurchbruch
DD ..... Deckendurchbruch
FBD ..... Fußbodendurchbruch
FDD ..... Fundamentdurchbruch
WS ..... Wandschlitz
WA ..... Wandaussparung
DA ..... Deckenaussparung
FBA ..... Fußbodenaussparung
RBL ..... Rohbaulichte
AL ..... Architekturlichte
STL ..... Stocklichte
GL ..... Glaslichte
STAM ..... Stockaußenmaß
DF ..... Drehflügel
DKF ..... Drehkippflügel
SF ..... Schiebeflügel
SWF ..... Schwingflügel
WF ..... Wendeflügel
HT ..... Hebetüre
HST ..... Hebeschiebetüre
T 30, T 60,
T 90 ..... Brandschutztüren mit Angabe der Brandwiderstandsklasse (siehe ÖNORM B 3850)
GT ..... gasdichte Türe
R 30 ..... rauchdichte Türe (siehe ÖNORM B 3855)
DT ..... Drucktüre

2.6 Rauch-, Abgas- und Luftfänge, Schächte

L ..... Lüftungsschacht
PT ..... Putztürchen
KT ..... Kehrtürchen
ABL ..... Abluft
ZUL ..... Zuluft
M ..... Müllabwurfschacht

geschoßweise Fangzuordnung (Bezeichnung des zugehörigen Anschlußgeschoßes, siehe auch ÖNORM B 8208):

K ..... Keller
E ..... Erdgeschoß
1 ..... 1. Obergeschoß (1. Stock)
2 ..... 2. Obergeschoß (2. Stock)
D ..... Dachgeschoß

[1]) Der Begriff "Oberkante" wurde als synonymer Begriff für "Oberseite" in dieser Norm belassen, weil er sehr verbreitet ist und in der Schnittdarstellung der Schnittkante zwischen Oberseite und Schnittebene entspricht.

2.5 Öffnungen und deren Abschlüsse

WD ..... Wanddurchbruch
DD ..... Deckendurchbruch
FBD ..... Fußbodendurchbruch
FDD ..... Fundamentdurchbruch
WS ..... Wandschlitz
WA ..... Wandaussparung
DA ..... Deckenaussparung
FBA ..... Fußbodenaussparung
RBL ..... Rohbaulichte
AL ..... Architekturlichte
STL ..... Stocklichte
GL ..... Glaslichte
STAM ..... Stockaußenmaß
DF ..... Drehflügel
DKF ..... Drehkippflügel
SF ..... Schiebeflügel
SWF ..... Schwingflügel
WF ..... Wendeflügel
HT ..... Hebetüre
HST ..... Hebeschiebetüre
T 30, T 60,
T 90 ..... Brandschutztüren mit Angabe der Brandwiderstandsklasse (siehe ÖNORM B 3850)
GT ..... gasdichte Türe
R 30 ..... rauchdichte Türe (siehe ÖNORM B 3855)
DT ..... Drucktüre

6.1 Stückgut (Mauerwerk), tragend oder nichttragend

(1) wärmedämmend, zB Ziegel(-decken), Hohlziegel, Leichtbetonsteine — hellrot

(2) ohne besondere Wärmedämmeigenschaft, zB Gipsdielen, Dünnwandsteine, Sichtziegel. — dunkelrot

6.2 Schüttgut, mit Füllmaterial, geschalt oder mit verlorener Schalung,
zB Plattenschalung oder Schalungssteine

(1) wärmedämmend, unbewehrt, zB Leichtbeton (-decken), Mantelbeton, Schalungssteine aus Wärmedämmaterial — violett

(2) ohne besondere Wärmedämmeigenschaft, mit vorrangig tragender Funktion, unbewehrt, zB Beton — hellgrün

(3) ohne besondere Wärmedämmeigenschaft, mit vorrangig tragender Funktion, jedoch bewehrt, zB Stahlbeton(-decken). — schwarz oder dunkelgrün

6.3 Dämmaterialien
Wärme- und Schalldämmschichten in Wänden und Decken, darstellbar nur bei entsprechendem Maßstab und entsprechender Schichtdicke.

(1) hart (begehbar), zB Schaumglas, Holzwolle-Dämmplatten — orange

(2) weich (nichtbegehbar), mineralische Faserdämmstoffe, Polystyrol-Partikelschaumstoff — orange

(3) vor Ort ausgeschäumt — orange

6.4 Betonfertigteile

(1) wärmedämmend violett — violett

(2) ohne besondere schwarz Wärmedämmung — schwarz

6.5 Holzkonstruktionen im Querschnitt

(1) gehobelt — hellbraun

(2) ungehobelt — hellbraun

6.6 Stahl (Metall)

6.7 Sperrschichten

6.8 Rollierung, Steinschüttung — beige

6.9 Boden

(1) bestehend (gewachsen) — dunkelbraun

(2) aufgeschüttet — dunkelbraun

6.10 Werkstein

(1) Kunststein — hellblau

(2) Naturstein — hellblau

Verordnung der Landesregierung über Baupläne (Bauplanverordnung)

Fundstellen der Rechtsvorschrift		
Datum	Publ.Blatt	Fundstelle
07.01.1993	LGBl	1993/01

Auf Grund des § 64 Abs. 4 in Verbindung mit Abs. 2 der Bauordnung für Wien, LGBl. für Wien Nr. 11/1930, in der Fassung der Gesetze LGBl. für Wien Nr. 12/1930, GBl. der Stadt Wien Nr. 1/1935 und 33/1936, LGBl. für Wien Nr. 17/1947, 45/1949, 16/1955, 28/1956, 14/1958, 31/1960, 16/1961, 3/1964, 10/1964, 9/1967, 13/1968, 6/1970, 15/1970, 25/1971, 6/1972, 28/1974, 18/1976, 11/1981,30/1984, 19/1986, 28/1987, 29/1987, 7/1990, 15/1991, 32/1991, 28/1992, 31/1992 und 34/1992 sowie der Kundmachung LGBl. für Wien Nr. 7/1960, 13/1985, 1/1986, 12/1986 und 8/1992 wird verordnet:

§ 1. (1) Die Baupläne müssen aus geeigneten, dauerhaft haltbaren Materialien bestehen. Die Abmessungen haben 210 mm x 297 mm zu betragen; größere Pläne sind nach diesen Abmessungen zu falten.

(2) Vervielfältigungen dürfen nur nach einem Zeichen-, Druck- oder gleichwertigen Kopierverfahren hergestellt werden. Sie müssen lichtecht und beständig sein.

§ 2. (1) Der Maßstab von Lageplänen hat 1:200 oder 1:500 zu betragen. Sind große Flächen darzustellen, ist auch ein anderer Maßstab zulässig.

(2) In jedem Lageplan ist die Nordrichtung zu kennzeichnen und der Maßstab anzugeben.

(3) Im Lageplan sind darzustellen:

1. neu zu errichtende Baulichkeiten und Bauteile — rot,
2. bestehende Baulichkeiten und Bauteile — grau,
3. abzutragende Baulichkeiten und Bauteile — gelb,
4. abzutragende und an derselben Stelle neu zu errichtende Baulichkeiten und Bauteile rotgelb schraffiert.

§ 3. (1) Das Bauvorhaben ist in Grundrissen, Schnitten und Ansichten im Maßstab 1:100 darzustellen. Soweit es zur Beurteilung erforderlich ist, sind wichtige Einzelheiten durch Sonderzeichnung in einem anderen geeigneten Maßstab auszuweisen. Der jeweilige Maßstab ist anzugeben.

(2) In den Grundrissen und Schnitten sind darzustellen:

1. neu zu errichtende Baulichkeiten aus
   a) Ziegelmauerwerk — rot,
   b) Beton — grün,
   c) Stahlbeton — schwarz,
   d) Stahl — blau,
   e) Holz — braun
   f) andere Baustoffe in einer anderen Farbtönung, die in einer Legende auszuweisen ist;
2. bestehende Bauteile — grau,
3. abzutragende Bauteile — gelb,
4. abzutragende und an derselben Stelle neu zu errichtende Bauteile in der in Z 1 festgelegten Farbe mit gelber Umrahmung.

(3) Neue Raumwidmungen und Raumflächen sind rot, aufgelassene gelb zu unterstreichen.

§ 4. Wenn es für die eindeutige Beurteilung notwendig ist, sind bei Abweichungen von bewilligten Bauvorhaben abzuändernde Grundrisse, Schnitte und Ansichten zur Gänze gelb zu durchkreuzen und die geplanten Abweichungen wie ein neues Bauvorhaben gesondert darzustellen.

§ 5. Diese Verordnung tritt mit 1. März 1993 in Kraft. Mit Inkrafttreten dieser Verordnung tritt die Verordnung der Wiener Landesregierung über den Maßstab, die Ausfertigung und die Beschaffenheit der Baupläne, LGBl. für Wien Nr. 44/1930, außer Kraft.

Die Bemaßung ist ein wesentlicher Bestandteil technischer Zeichnungen. Zur Bemaßung sind Festlegungen über die Darstellung von Bemaßungsbegriffen, die Eintragung von Maßzahlen und die Wahl von Maßeinheiten notwendig.

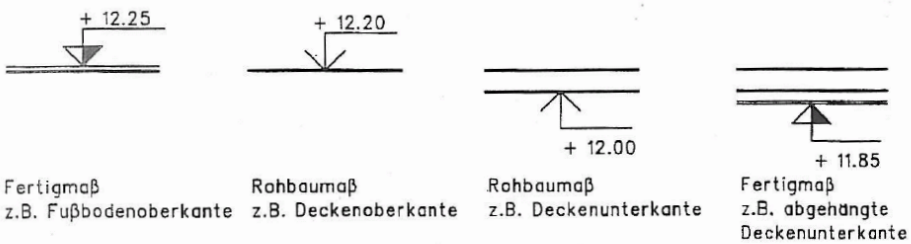

Bild 13: Beispiele für Höhenangaben in Vertikalschnitten

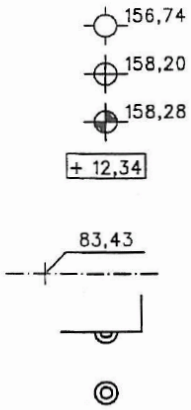

Höhenlage eines Punktes im Gelände

Höhenlage eines Punktes in einem Bauwerk – Rohbaumaß

Höhenlage eines Punktes in einem Bauwerk – Fertigmaß

Höhenlage einer waagrechten Fläche.

Höhenlage eines Punktes an einer Linie, z.B. Bruchkante, Grabensohle, Leitung jeder Art, insbesondere sind die Höhen von Gefällsbrüchen, Richtungsänderungen, Abzweigungen und Vereinigungen, End– und Anfangspunkten anzugeben

Höhenfestpunkt an Bauwerken (Mauerbolzen), eventuell mit Angabe der Punktnummer

Höhenfestpunkt (auch Nivellementstein); Nivellementpunkt, eventuell mit Angabe der Punktnummer

In bestimmten Fällen sind in die Grundrisse auch Höhenmaße als Längenmaße einzutragen, wobei ebenfalls Abkürzungen verwendet werden:

RPH 80 (= Rohbauparapethöhe 80 cm über FBOK)

FPH 85 (= fertige Parapethöhe 85 cm über FBOK)

STH 25 (= Sturzhöhe 25 cm bzw. Rohbausturzunterkante bis Rohbaudeckenunterkante).

Maßart	Planart	Maßinheit
Längenmaße	Lagepläne (M 1:200, 1:500) Einreichpläne M 1:100 Ausführungspläne M 1:50 – 1:1	Meter (m) Zentimeter (cm) Zentimeter (cm)
Höhenangaben (Koordinaten)	in allen Planarten	Meter (m)
Rohrquerschnittsmaße (Durchmesser)	in allen Planarten	Millimeter (mm)
Stahlprofilquerschnittsabmessungen	in allen Planarten	Millimeter (mm)
Winkelmaße	in allen Planarten für Steigungen oder Gefälle	Grad (°) [1] Neugrad (^{g})[2] Radiant (rad) [3] Prozent (%) Promille (‰) Dreieckskatheten

1) 1° = 1/90 des rechten Winkels
2) 1^g = 1 Gon = 1/100 des rechten Winkels
3) rad = Kreisbogenlänge/Radius
360° = 2p rad

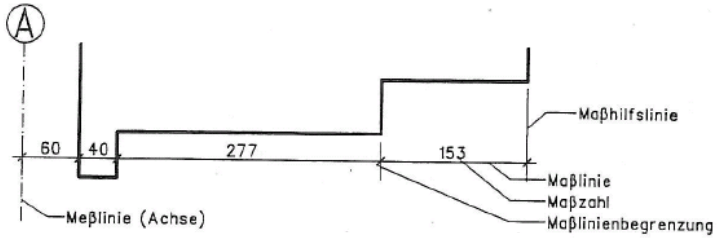

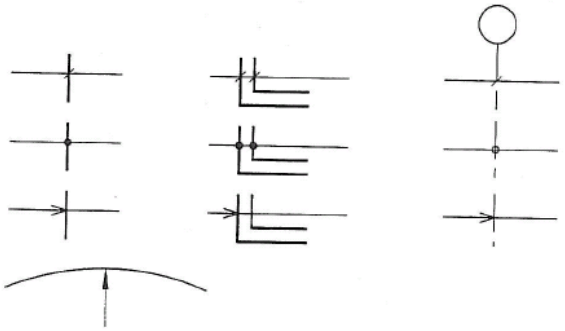

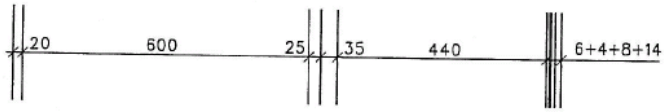

Planinhalte

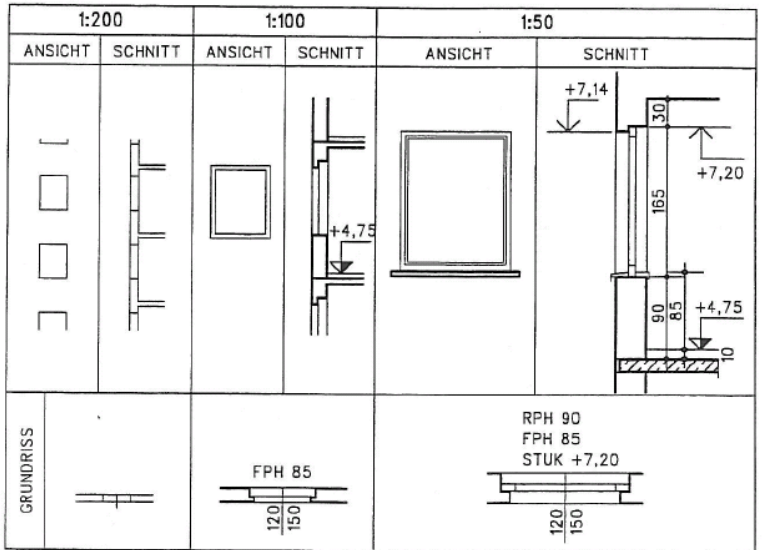

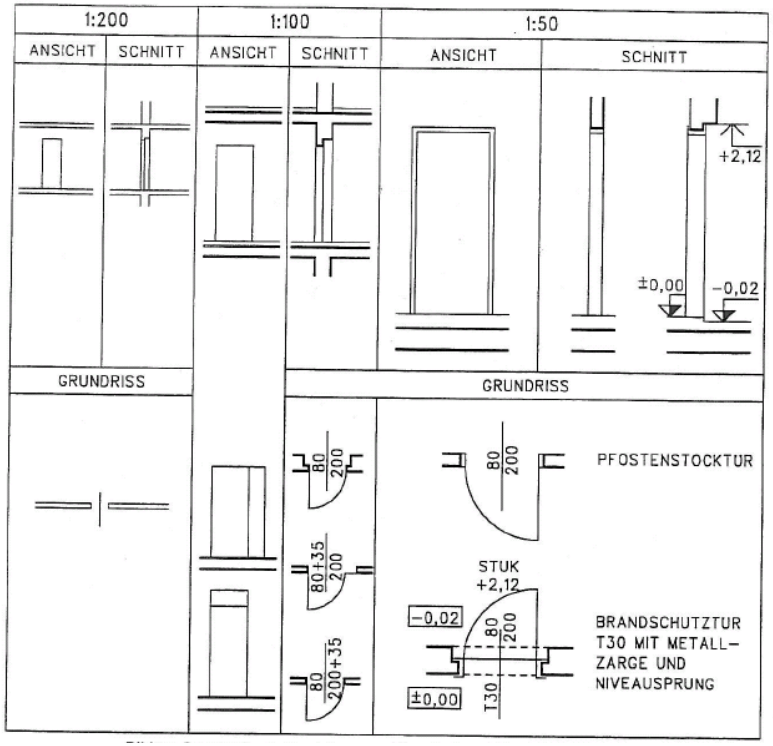

Planinhalte

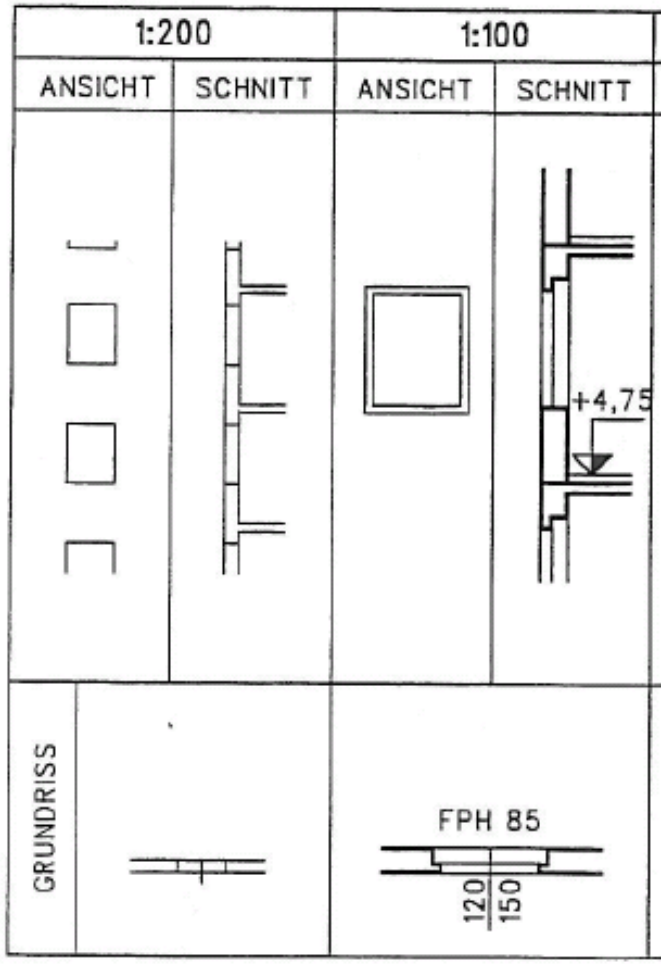

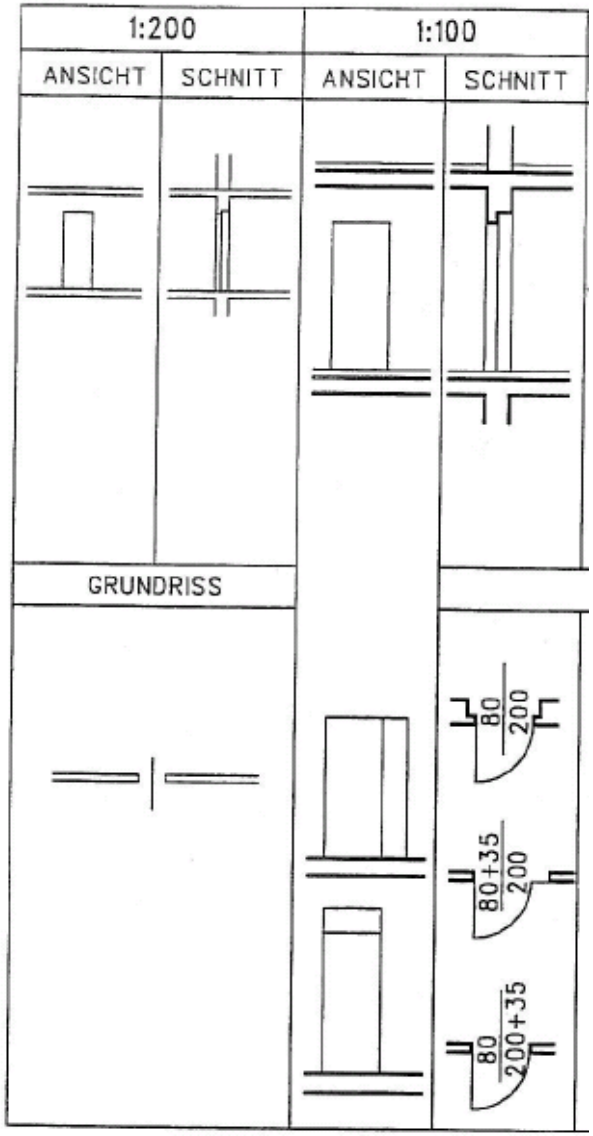

Planinhalte

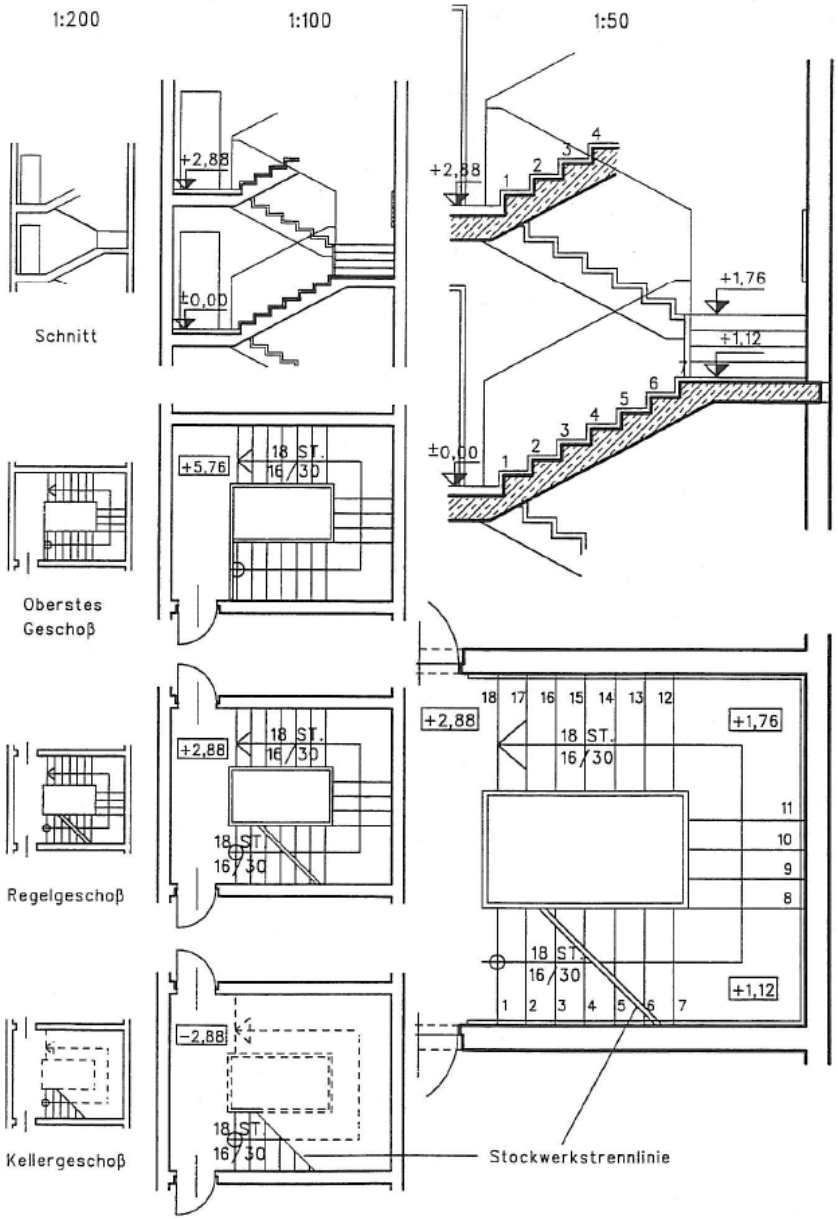

Planinhalte

1:200 1:100 1:200 1:100

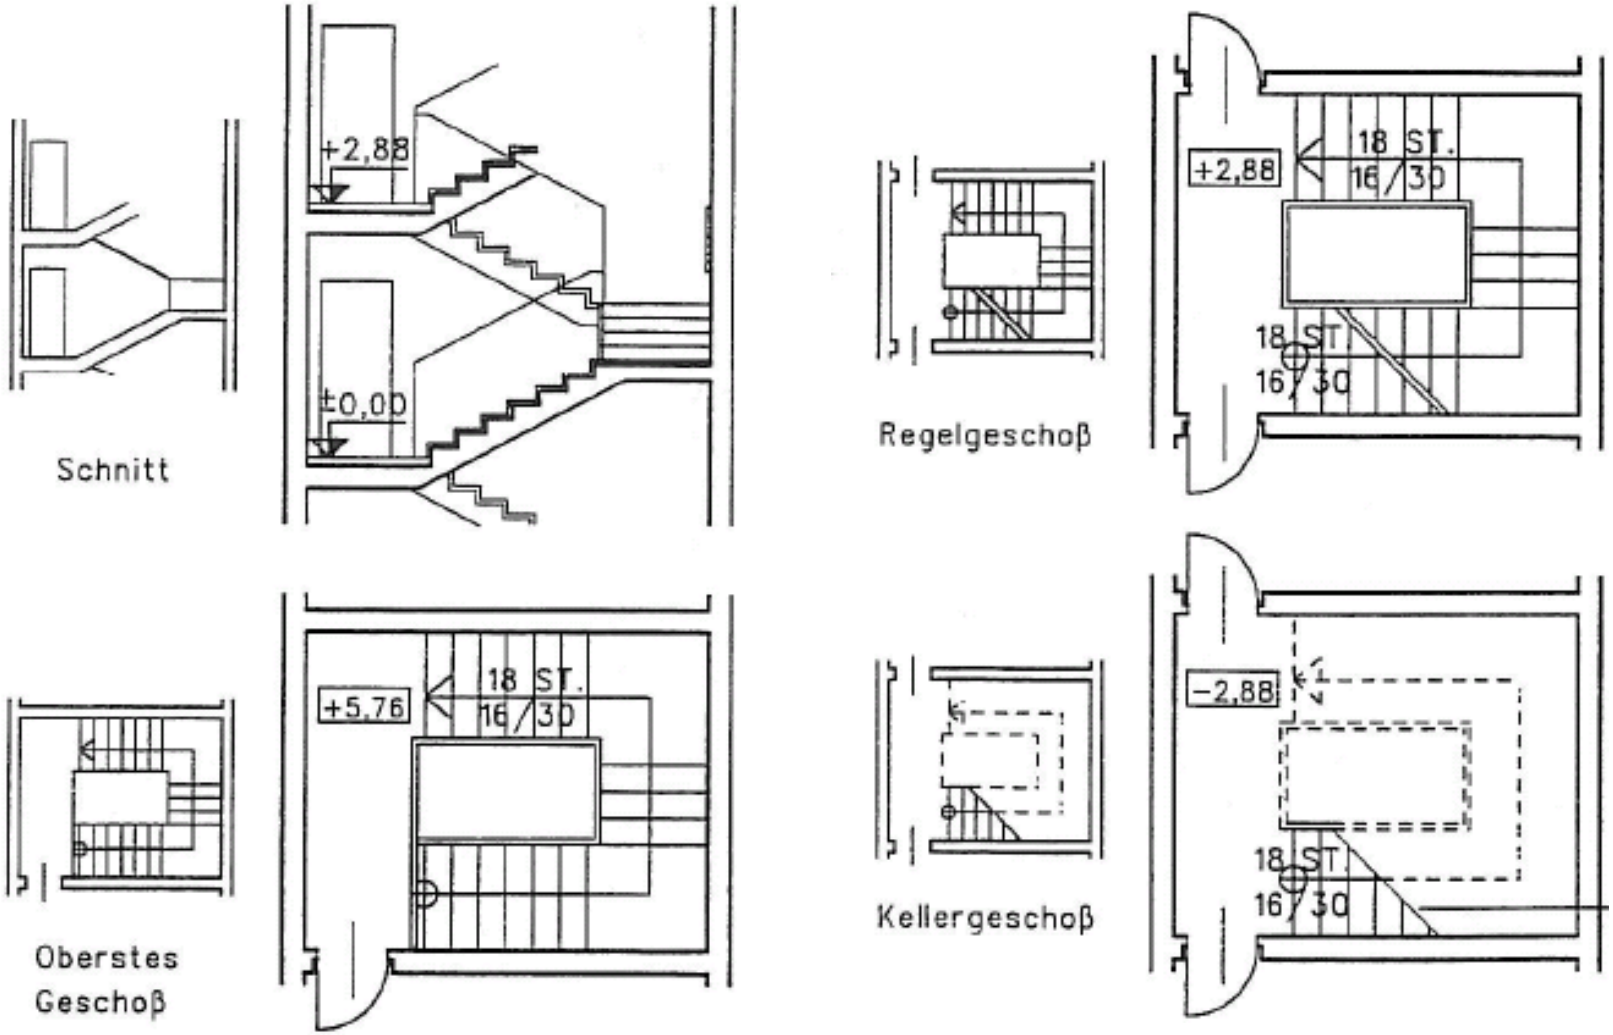

Planinhalte

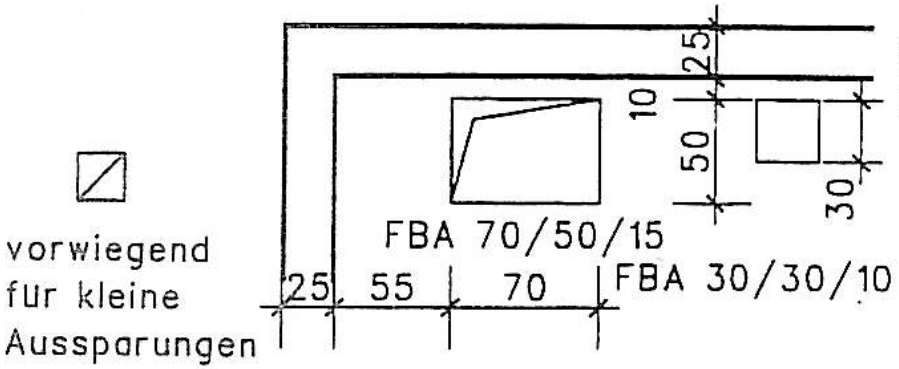

Fußbodenaussparung im Grundriß
Erforderliche Angaben:
(1) Symbole
(2) Angabe des Querschnittes u. der Tiefe
(3) Lagekotierung

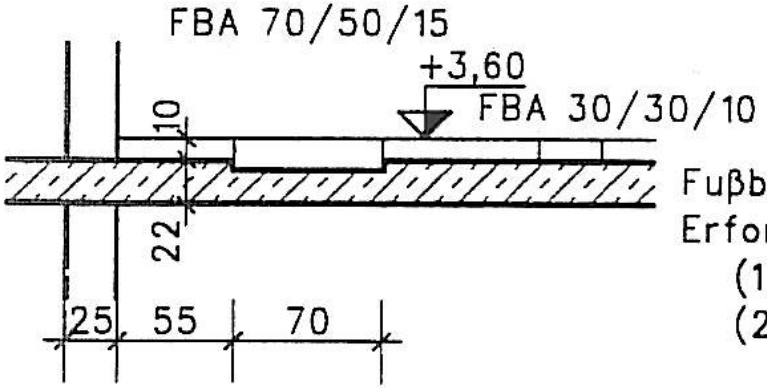

Fußbodenaussparung im Schnitt
Erforderliche Angaben:
(1) Angabe des Querschnittes u. der Tiefe
(2) Lagekotierung

Planinhalte

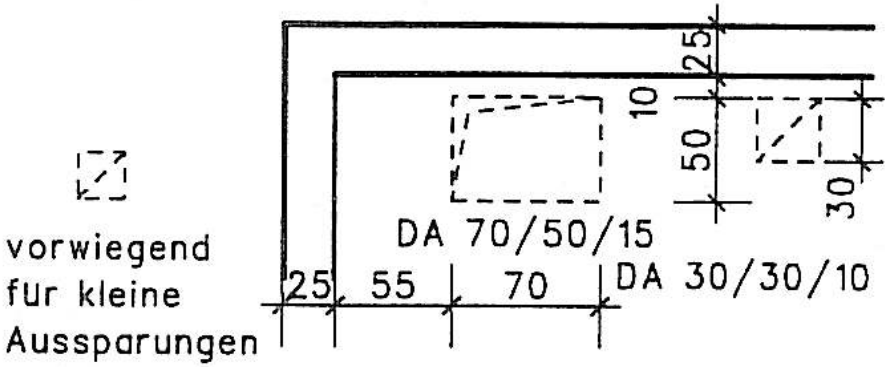

Deckenaussparung an der Unterseite
der darunter liegenden Decke
Erforderliche Angaben:
(1) Symbole
(2) Angabe des Querschnittes u. der Tiefe
(3) Lagekotierung

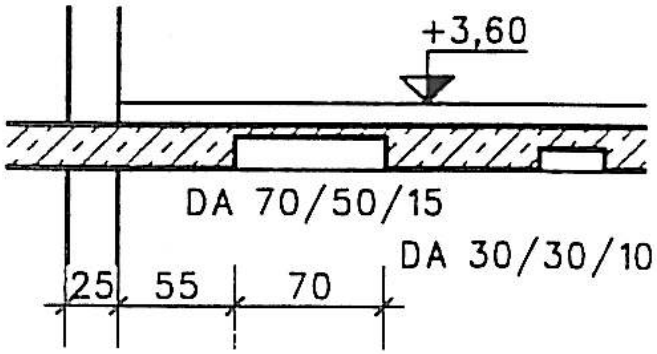

Deckenaussparung im Schnitt
Erforderliche Angaben:
(1) Angabe des Querschnittes u. der Tiefe
(2) Lagekotierung

Planinhalte

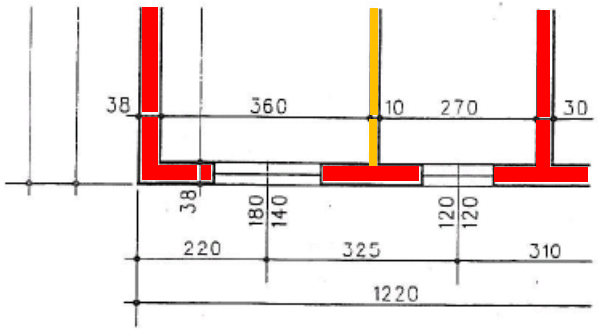

Einreichplan; M=1:100; Massivbau

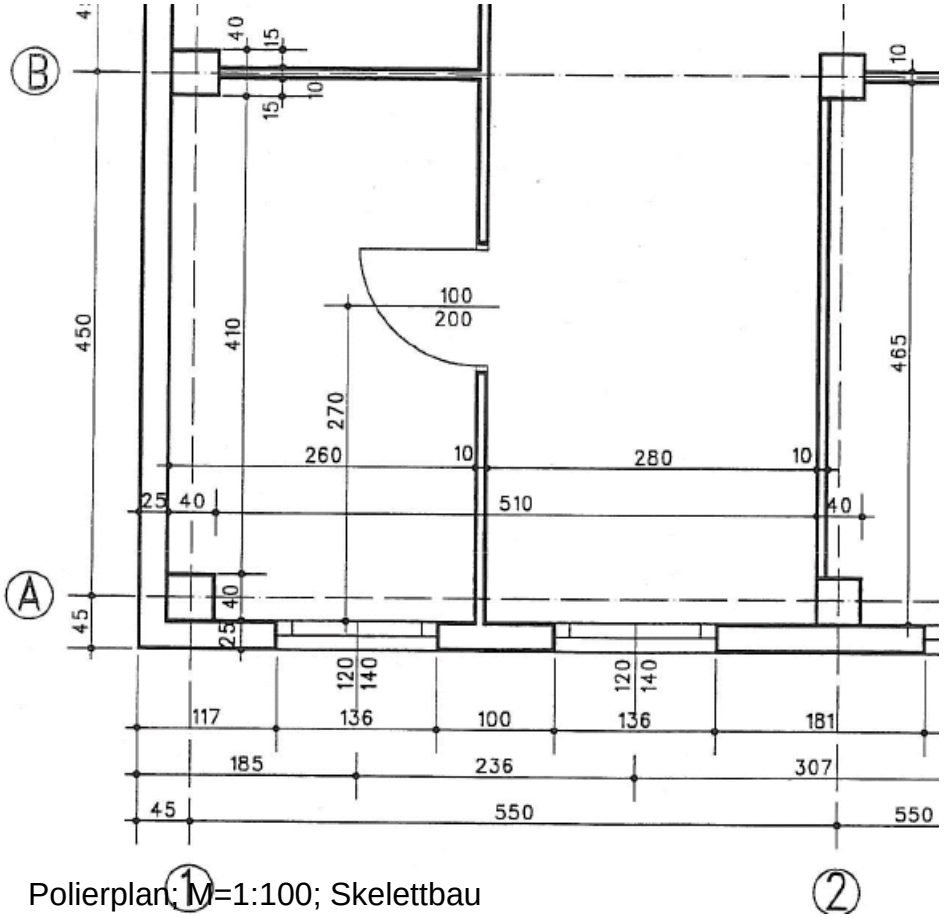

Polierplan; M=1:100; Skelettbau

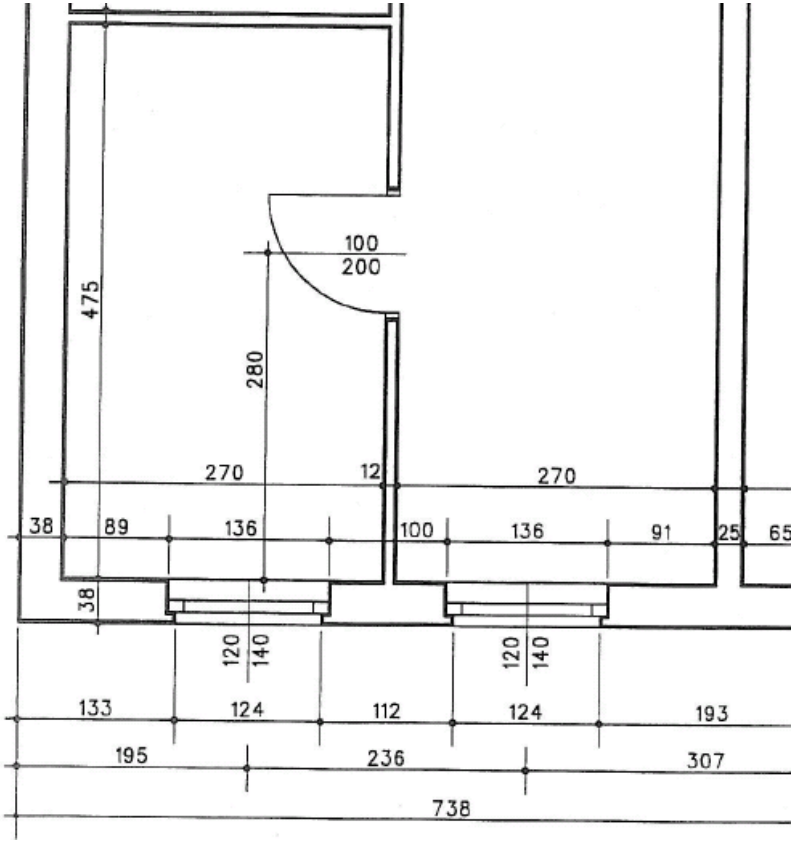

Polierplan; M=1:100; Massivbau

Beispiele/Anwendungen

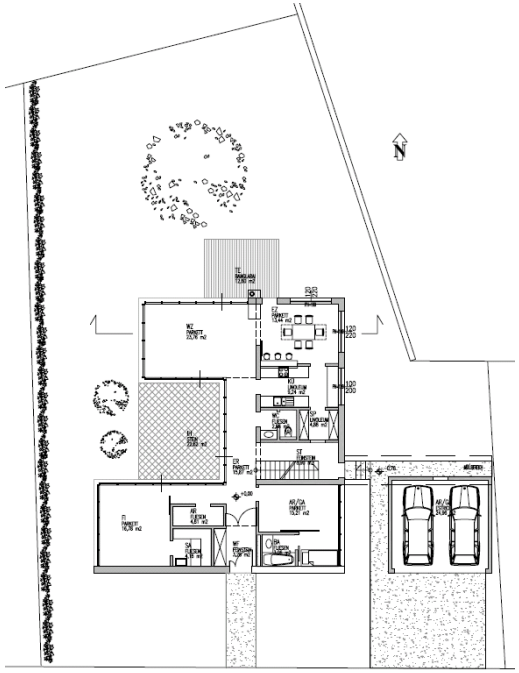

Entwurfsplan; Lageplan
M=1:250

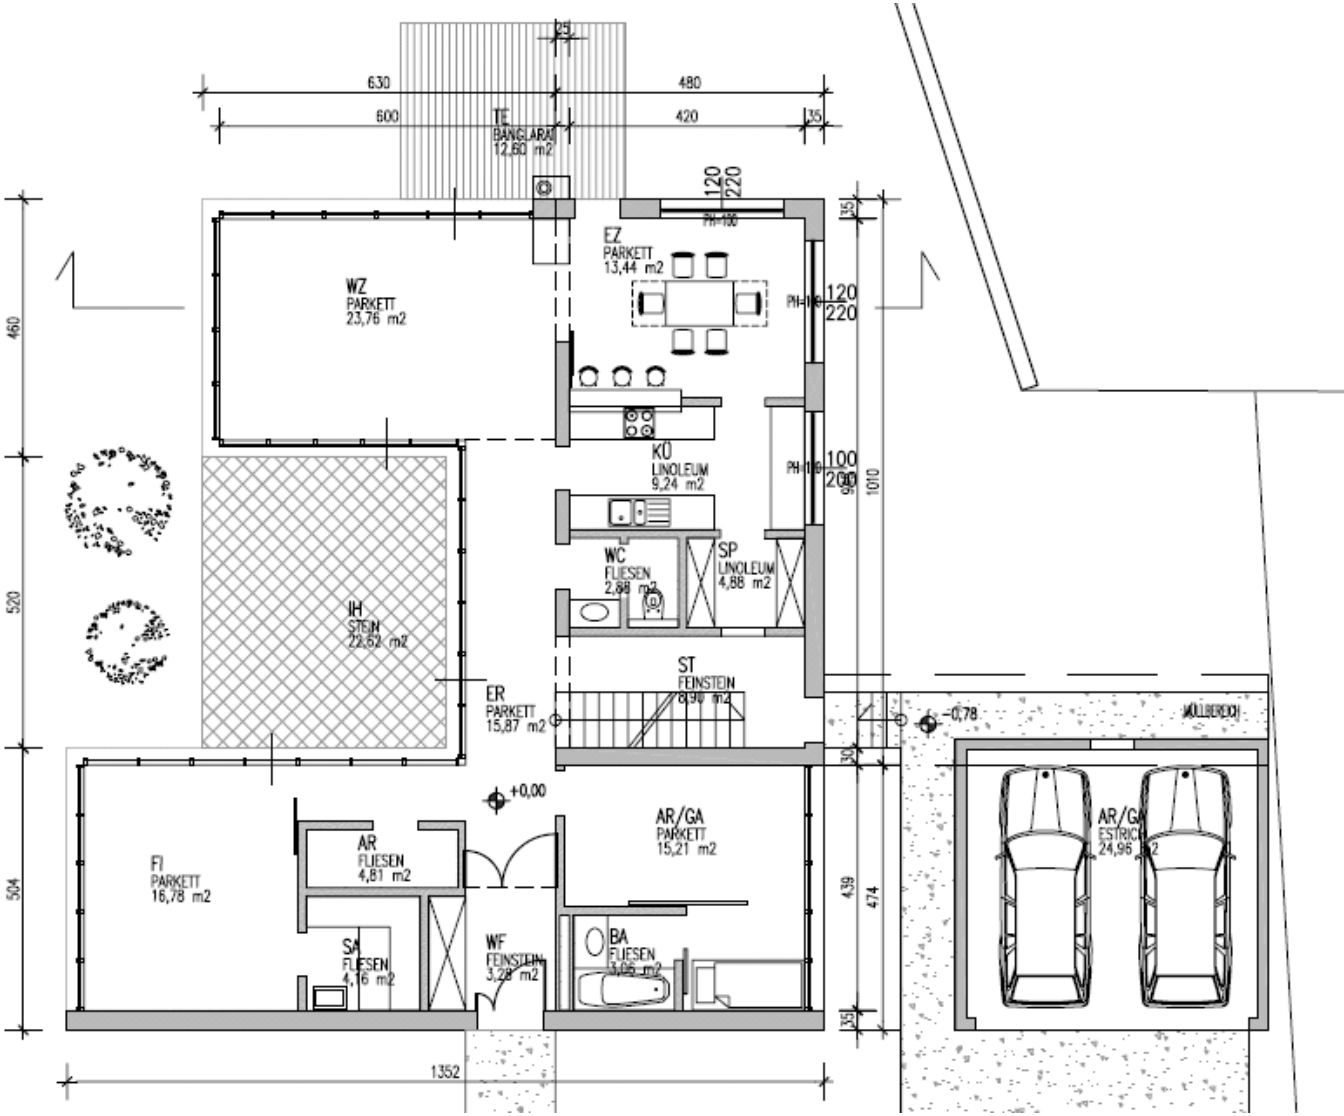

Entwurfsplan; Grundriss
M=1:100

Beispiele/Anwendungen

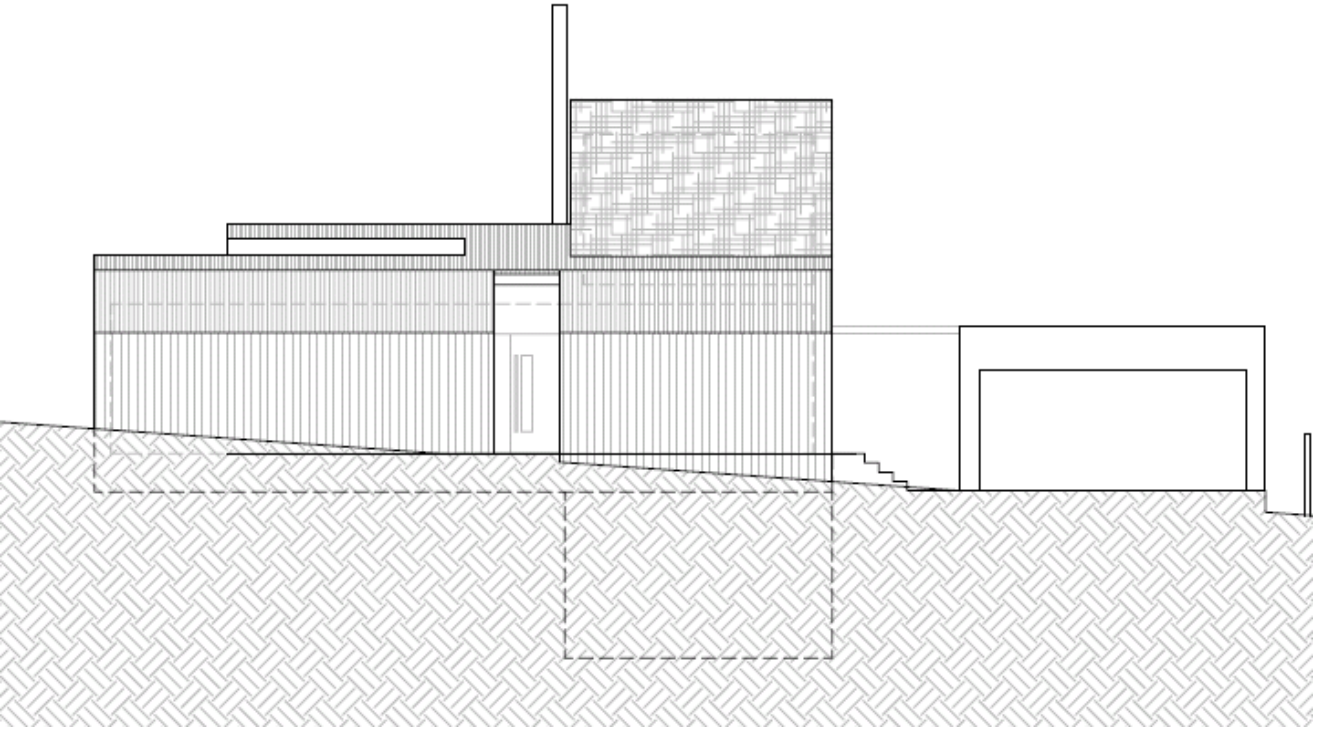

Entwurfsplan; Ansicht
M=1:100

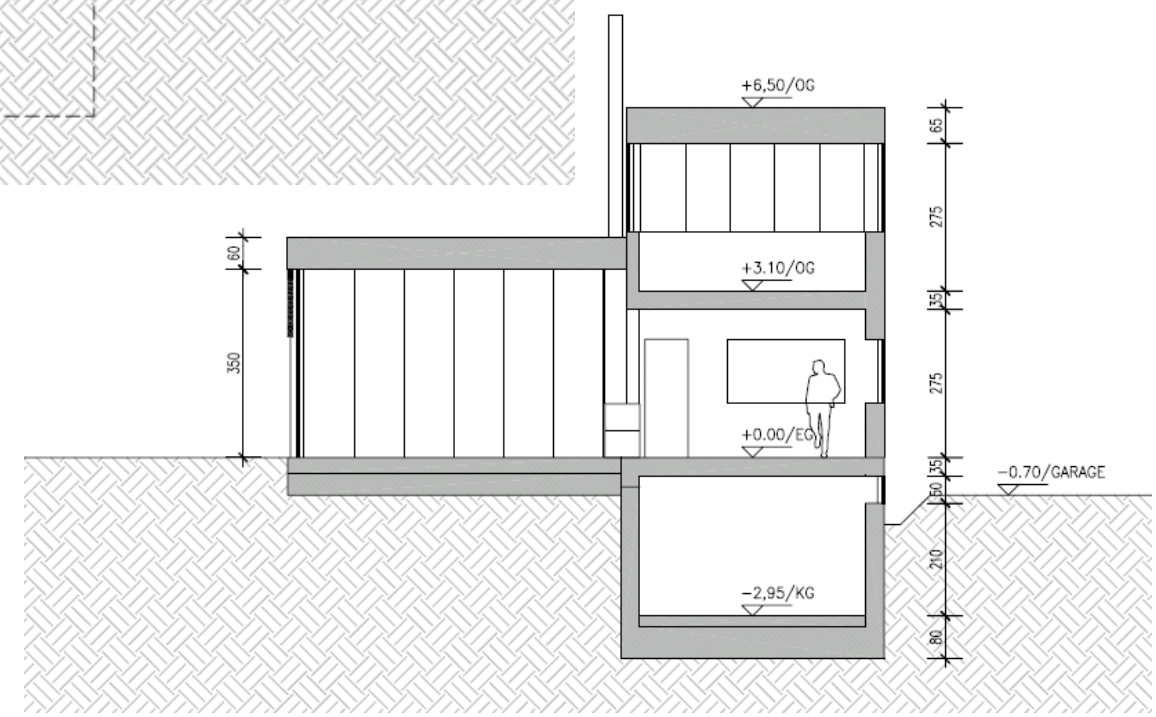

Entwurfsplan; Schnitt
M=1:100

Beispiele/Anwendungen

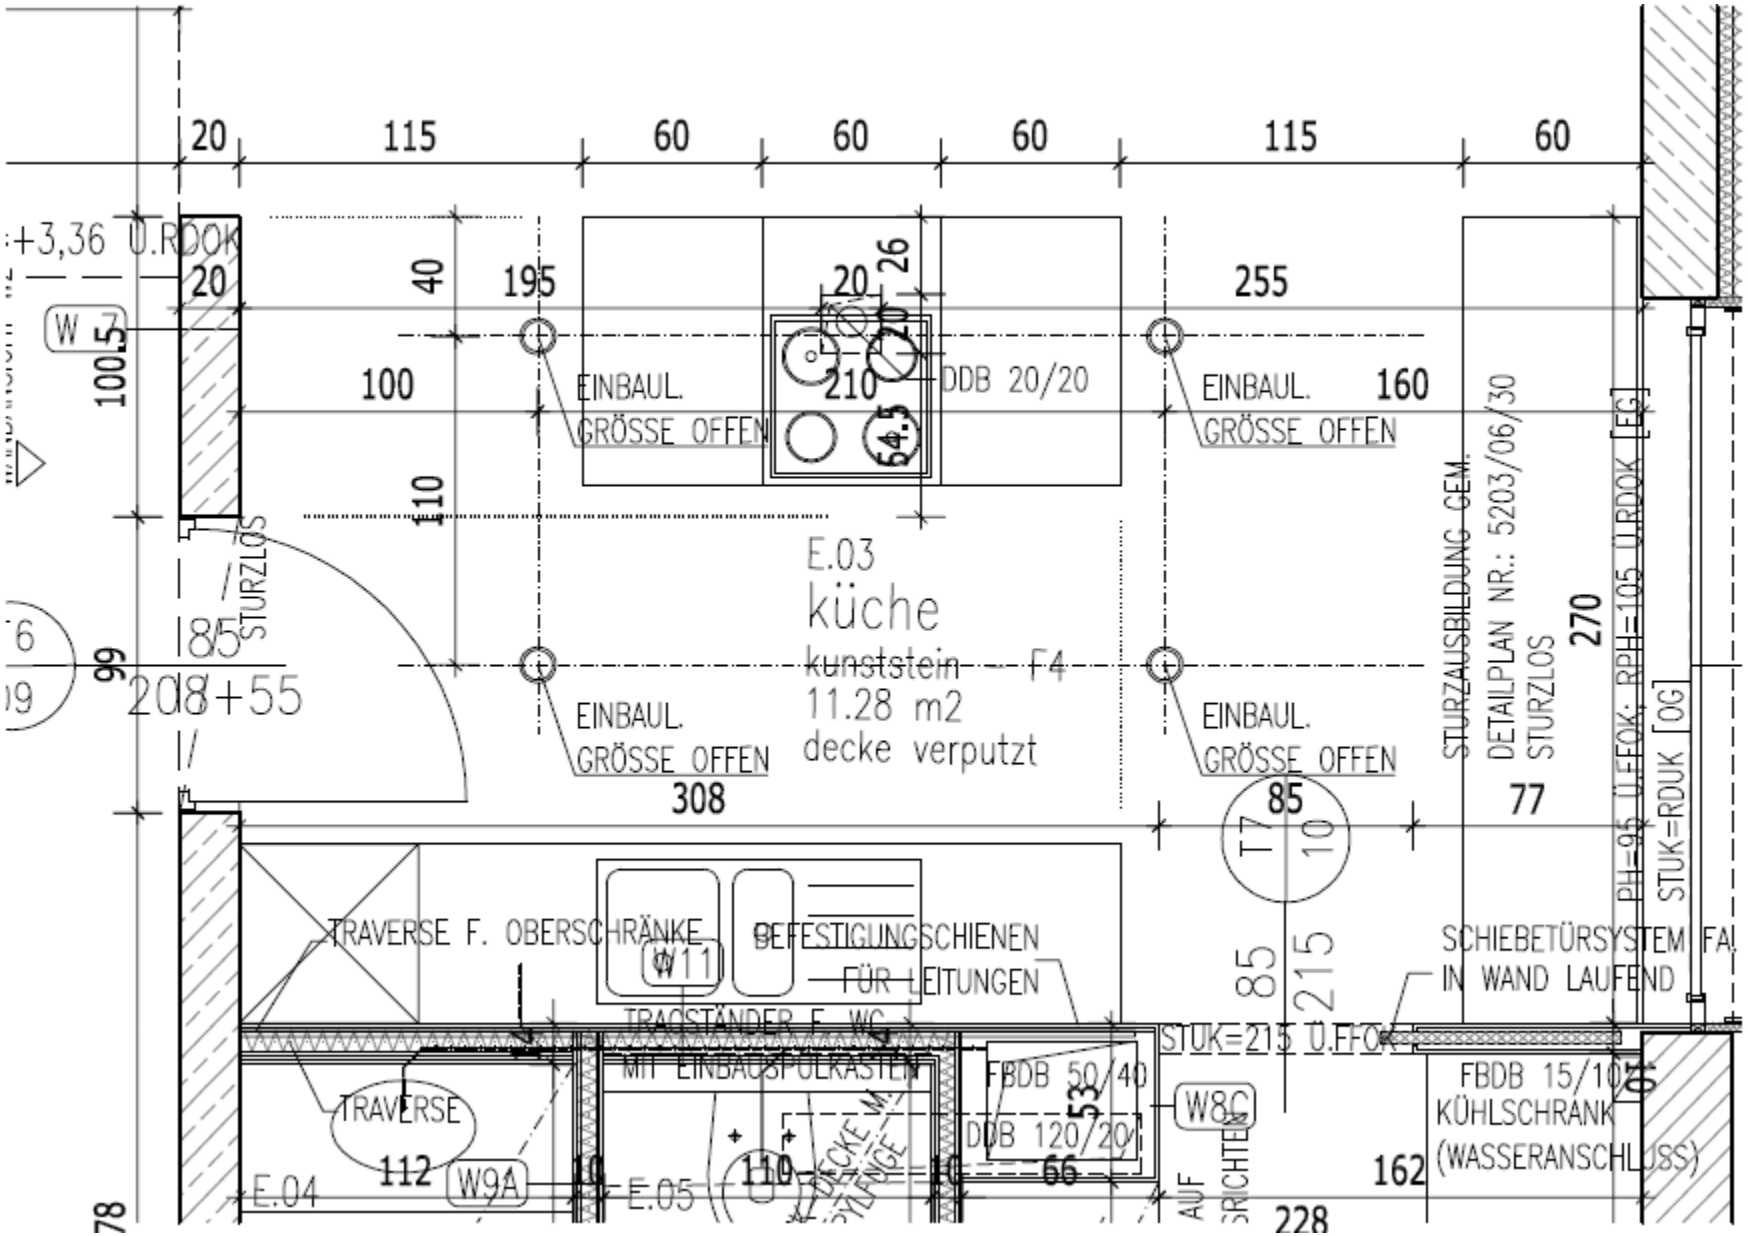

Ausführungsplan; Deckenspiegel Küche
M=1:50